


TEMPORARY HALF-PIPE SKATE RAMP - SECTION, ELEVATION AND PLAN

Ref TW-HP-001 Rev P01 4 October 2026 All dimensions in metres. 1:50, 1:100, 1:200 at A3

NOT A DESIGN - NOT FOR CONSTRUCTION - NOT A PERMIT TO LOAD

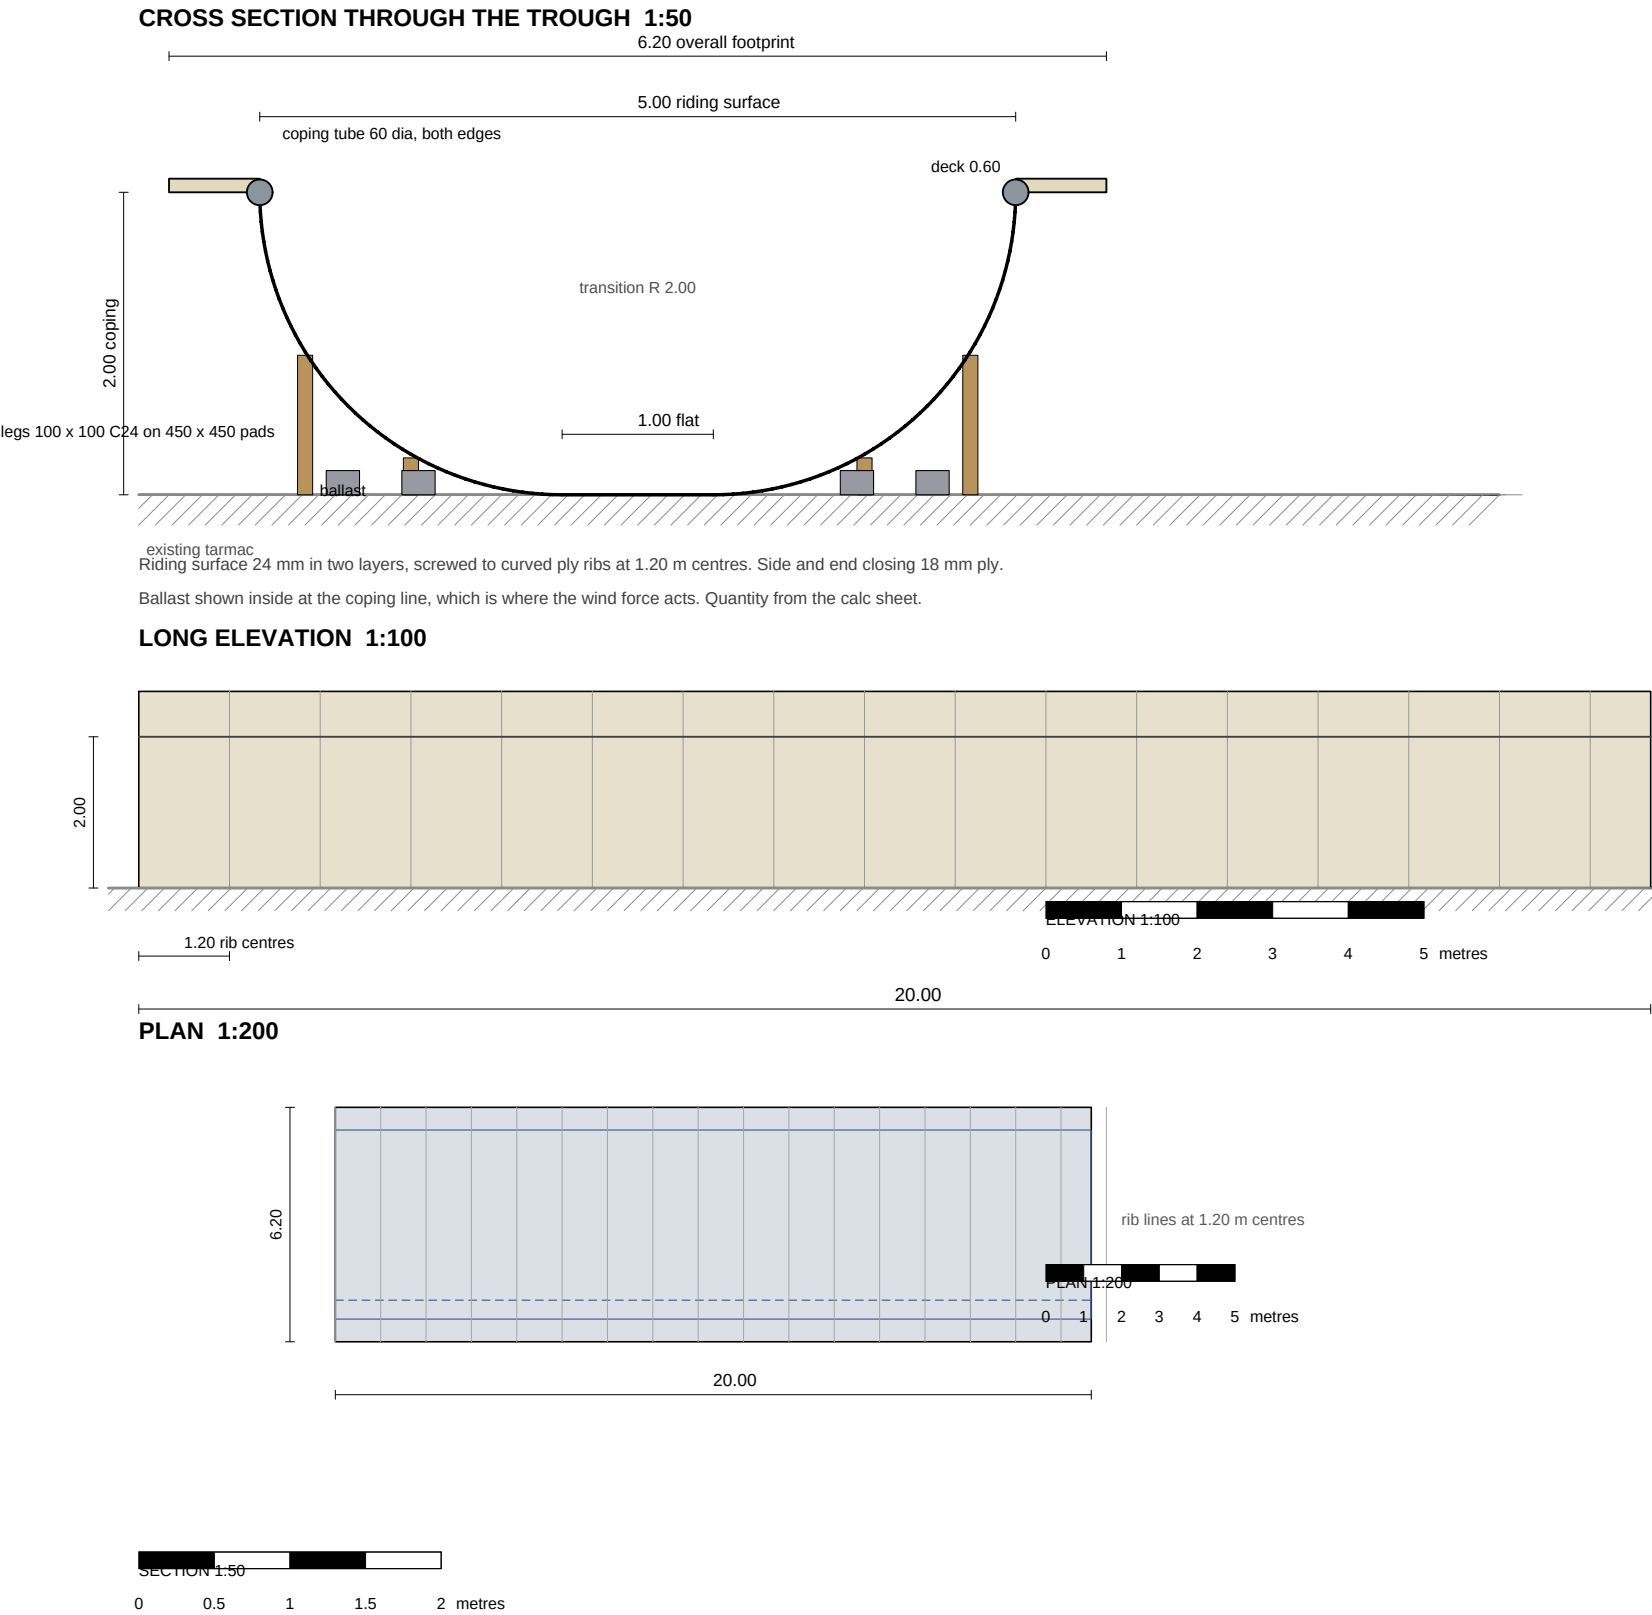

WHAT THIS IS

A temporary half-pipe 20.00 m long with 5.00 m of riding surface: a 1.00 m flat bottom between two 2.00 m transitions, so the coping stands 2.00 m high. Decks 0.60 m each side, 6.20 m overall footprint.

Framing: 100 x 100 C24 legs on 450 x 450 spreader pads, 100 x 75 bearers laid flat, curved ply ribs at 1.20 m centres, 24 mm ply riding surface in two layers.

IT HAS TO BE HELD DOWN. The ramp presents a 40 m2 face to the wind - ballast in the order of 3 to 7 tonnes, or ground anchors. See the calc sheet. Nothing is ridden until that is designed, checked and permitted.

THE STANDARDS THAT GOVERN IT

- BS EN 14974:2019**
- Skateparks - safety requirements and test methods. THE product standard for a facility used by the public on skateboards, roller sports and BMX. Supersedes BS EN 14974:2006+A1:2010.
- BS EN 13814-1:2019+A1:2024**
- Safety of amusement rides and amusement devices - design and manufacture. Applies to mobile and temporary devices: if the ramp is hired in as an attraction this is the design standard.
- BS EN 1991-1-4**
- Wind actions, where the designer works to Eurocode rather than the simplified method.
- BS 5975-1:2024 / BS 5975-2:2024**
- Temporary works procedure: roles, register, check categories, permits. Replaced BS 5975:2019.
- CDM 2015**
- Principal Contractor duties, the design brief, and the temporary works register.
- BS EN 1090-1**
- Execution of steel structures - if the coping, anchors or frame are fabricated steel.

Nothing is erected, ballasted or ridden until a competent temporary works designer has designed and checked it and a permit to load is issued.

SECTION, ELEVATION, PLAN		Rev P01
Project	Temporary half-pipe skate ramp	
Drawing	1 of 1	
Reference	TW-HP-001	
Date	4 October 2026	
Drawn	Banksy, for Dal Hopwood	
Scale	1:50, 1:100, 1:200 at A3	
NOT FOR CONSTRUCTION - NOT A DESIGN - NOT A PERMIT TO LOAD		